


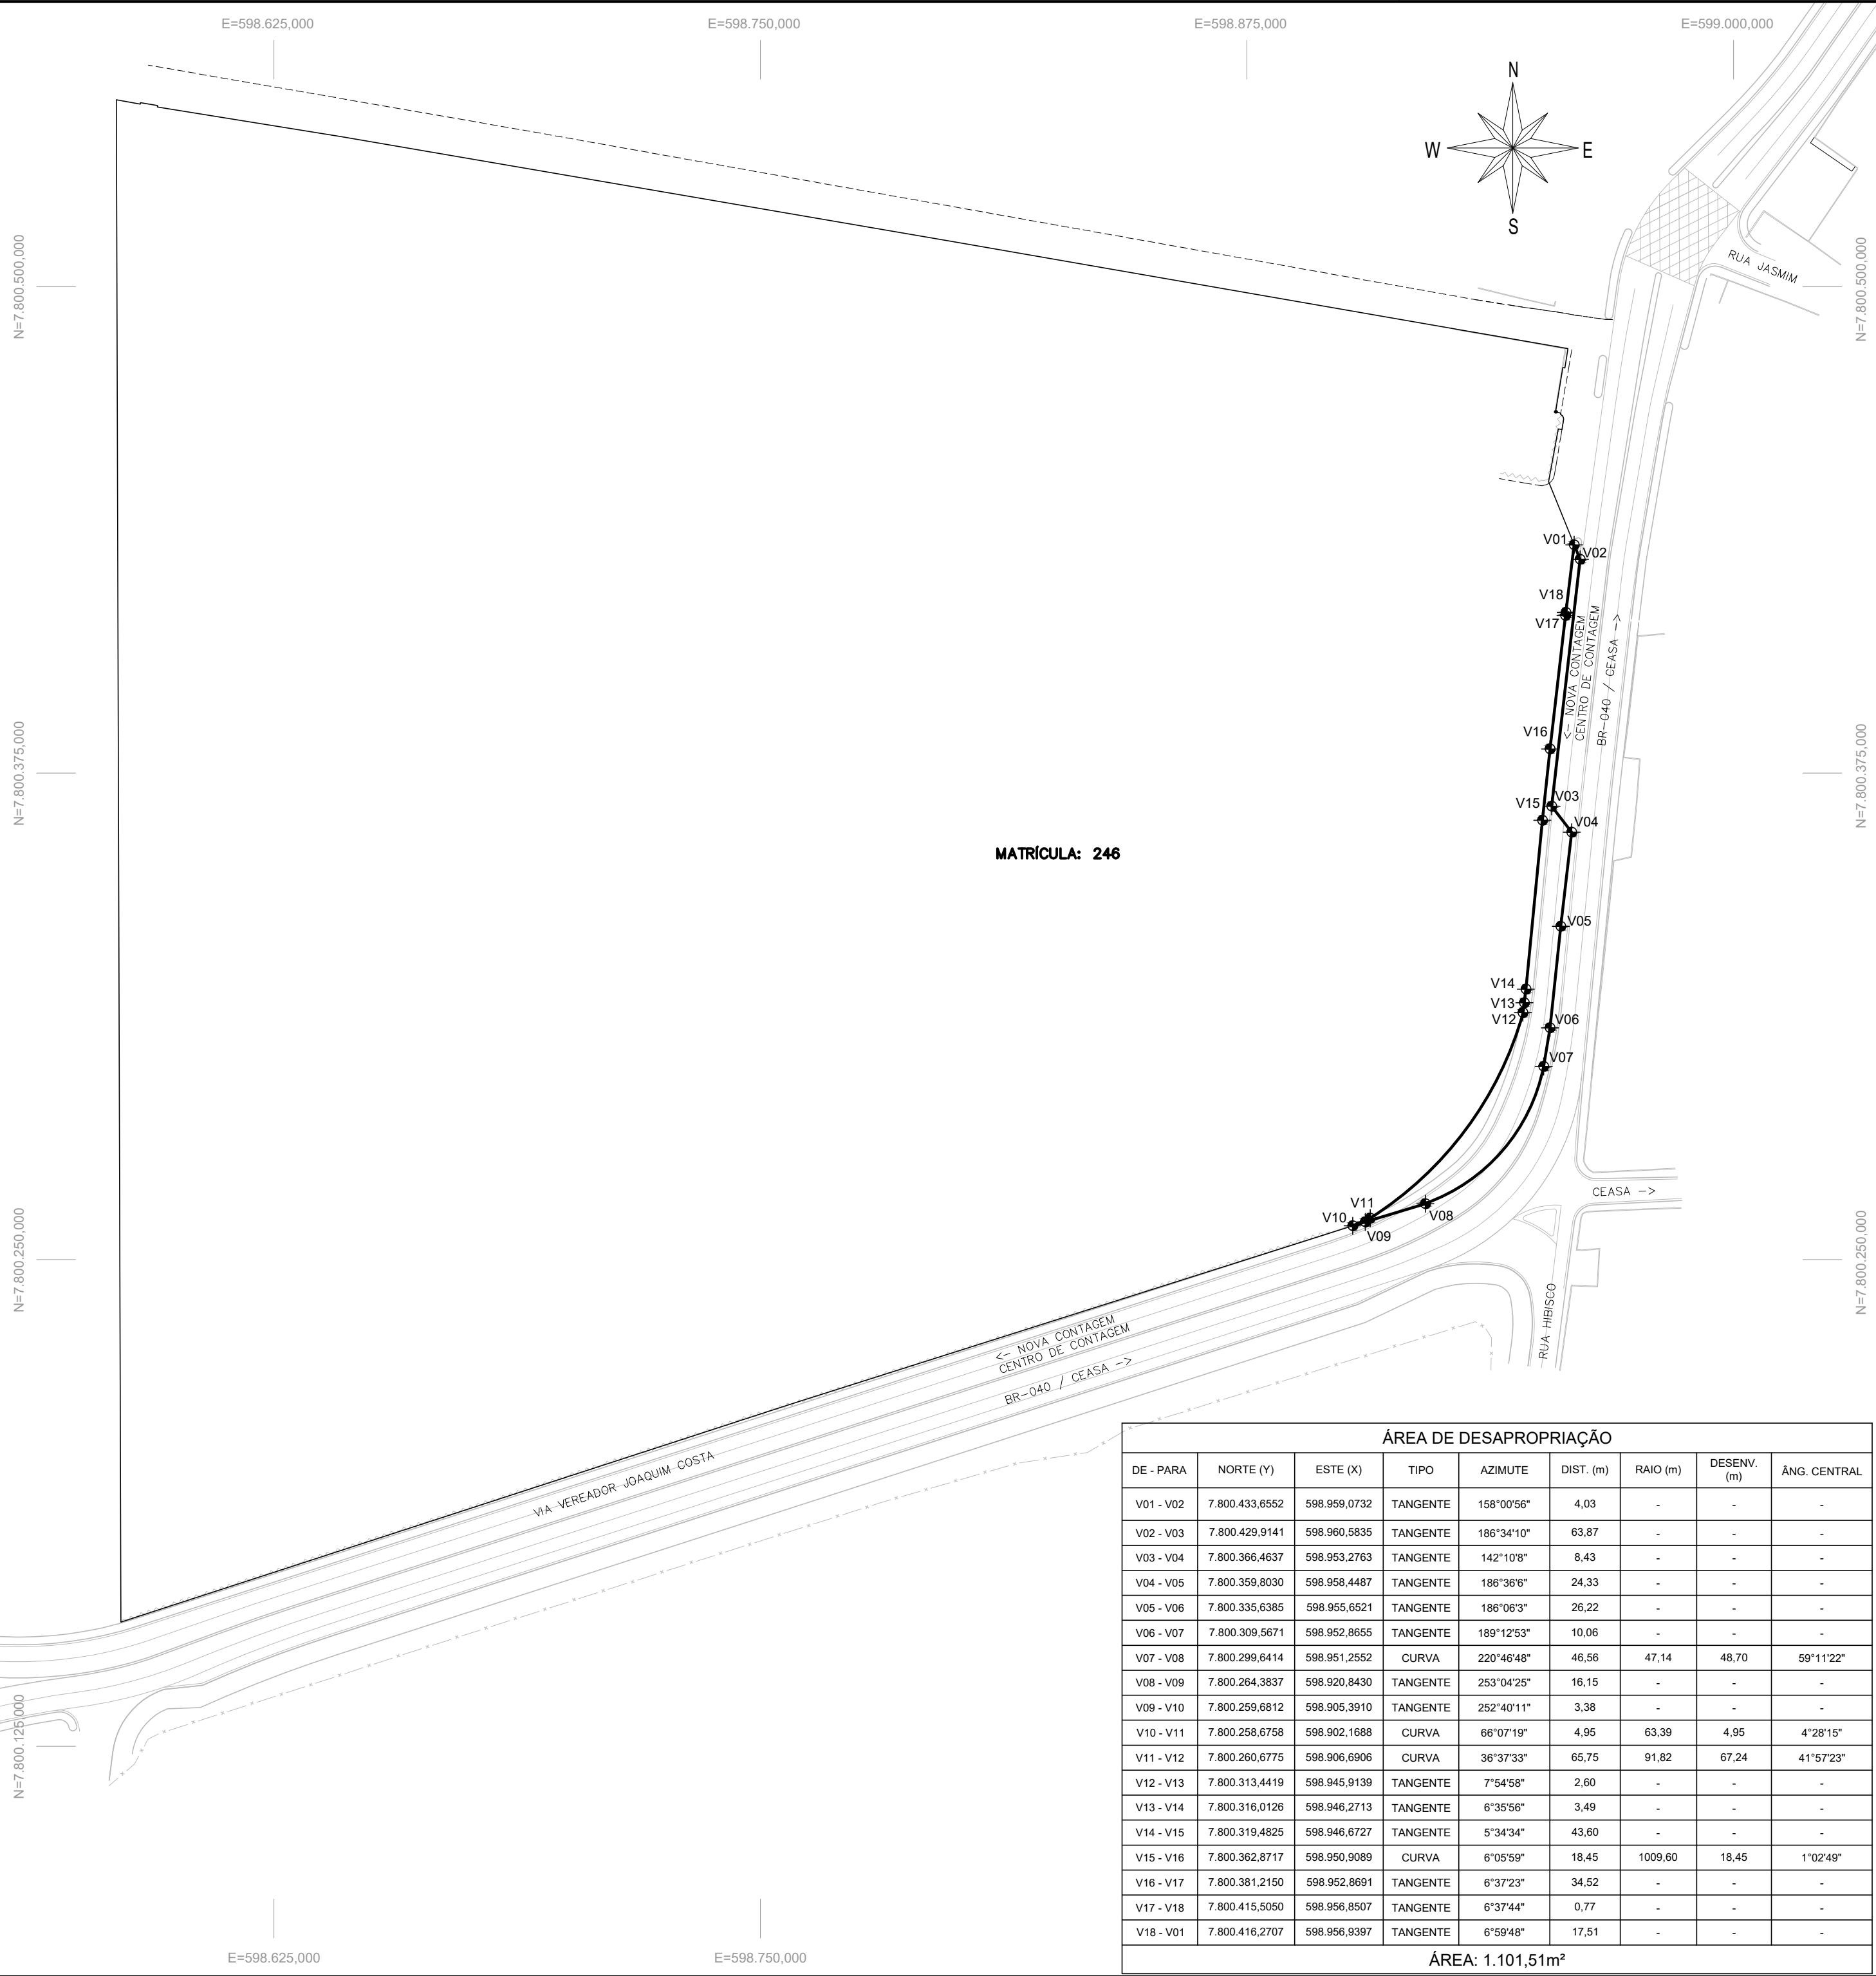

NOTAS:

1- GERAL
1.1- TODAS AS UNIDADES DE MEDIDA ESTÃO EM METRO, EXCETO QUANDO INDICADA.

TABELA RESUMO:

MATRÍCULA 246		
ÁREA TOTAL (m²)	DESAPROPRIADA (m²)	REMANESCENTE (m²)
110.855,41	1.101,51	109.753,90

CONTROLE DE EMISSÕES:

REVISÃO	DATA	ASS.	DESCRIÇÃO
R00	05/06/2026	FANY ANDRADE	EMIÇÃO INICIAL

CONTRATADA
TOPGEO CONSULTORIA LTDA
CNPJ: 01.208.058/0001-98
topgeo@topgeo.com.br

TOPGEO
Rua Fernandes Tourino, 929 - 1201,
Laudes, Belo Horizonte-MG
C E P : 3 0 . 1 1 2 - 0 0 3

CONTRATANTE

RESPONSÁVEL TÉCNICO

LUÍS HENRIQUE SOUZA
Luís Henrique Araújo Lima de Souza
ENGENHEIRO CIVIL CREA-MG 249.258/D

PROPRIETÁRIO

ATIVIDADE TÉCNICA
MEMORIAL DESCRITIVO DA ÁREA A SER DESAPROPRIADA

ENDEREÇO
VIA VEREADOR JOAQUIM COSTA
CONTAGEM - MG

CONTRATO
1693

ART
-

EMPREENDIMENTO
AMPLIAÇÃO DO SISTEMA VIÁRIO

TÉCNICO/PROJETISTA

FANY ANDRADE
Jestefania Aparecida de Andrade
ENGENHEIRA CIVIL CREA-MG 246.102/D

CORRESPONSÁVEL

HANDERSON ARAÚJO
Handerson Araújo de Souza
ENGENHEIRO CREA-MG 69.254/D

PLANO PROJEÇÃO	DATUM	FUSO	FORMATO	ESCALA	PRANCHA
UTM	SIRGAS 2000	SF 23 (MC -45°)	A2	1:1250	01/01

G:\Drives compartilhados\Z_Topgeo_Tambasa\Projetos\1693-TPG_Tambasa\Acesso viário\Desapropriação\G1696_V00-DES-R00-Planta Geral Matrícula 246.dwg